

# Художественный проект

Интерьер квартиры по адресу:  
г.Москва,

Заказчик:




Москва 2021


КОНЦЕПТУАЛЬНЫЙ ПРОЕКТ

## Список чертежей

N п.п.	Наименование	
РЧ-1	План обмеров.	2 шт.
РЧ-2	План демонтажа и возводимых стен, площади помещений.	2 шт.
РЧ-3	План пола. Отметки, отделочные материалы	2 шт.
РЧ-4	План расстановки мебели, примечания.	2 шт.
РЧ-5	План потолка. Отметки, привязки светильников.	2 шт.
РЧ-6	План отделки стен и потолков декор. элементами. Спецификация декора.	2 шт.
РЧ-7	Ведомость отделки	2 шт.

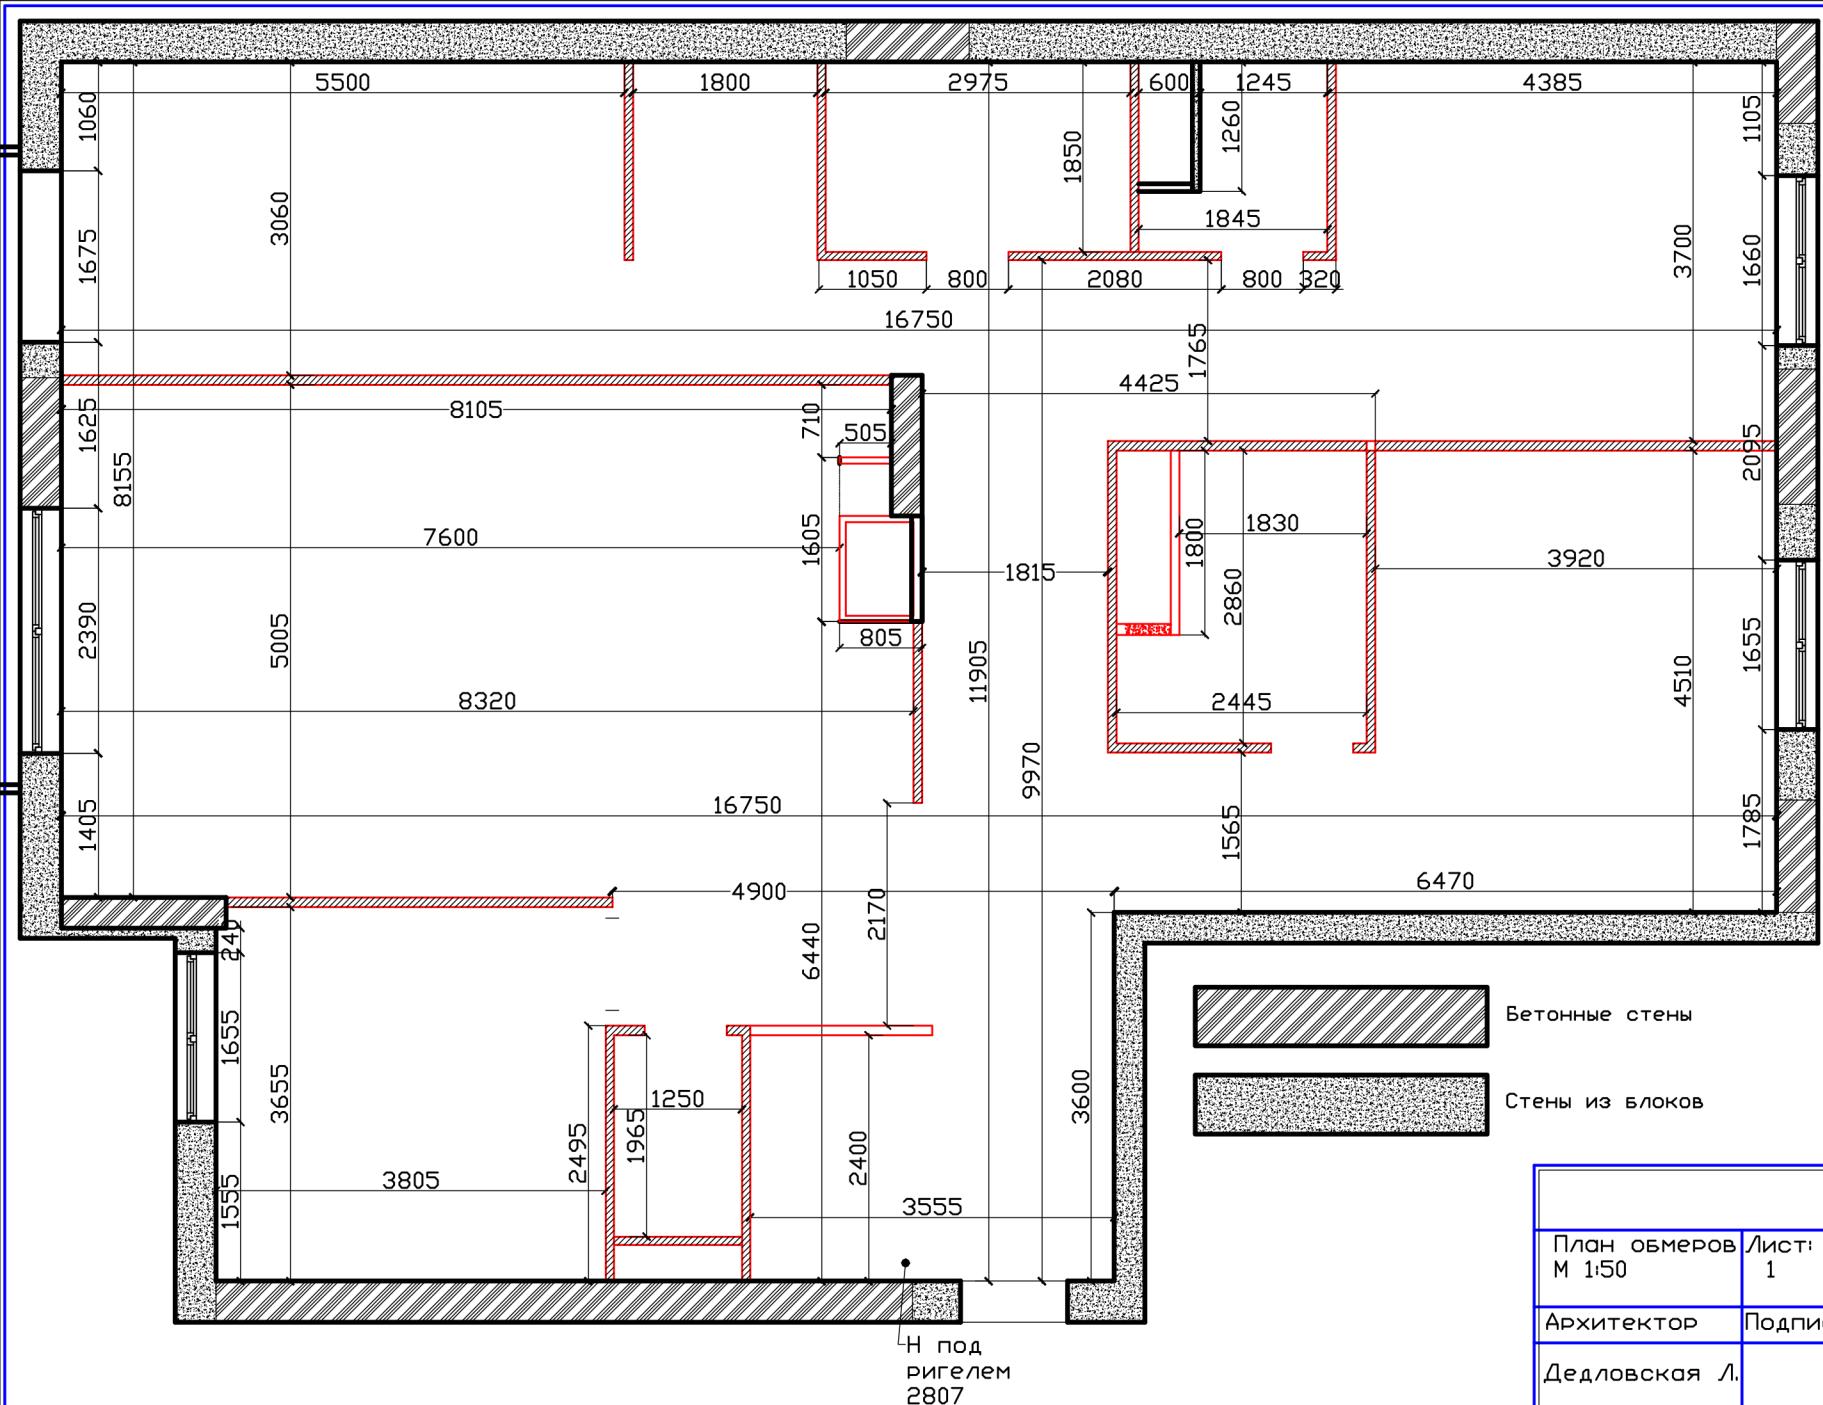

План обмеров		
М 1:50	Лист:	Листовъ
Архитектор	Подпись	Дата:
Дедловская Л.		24.12.19

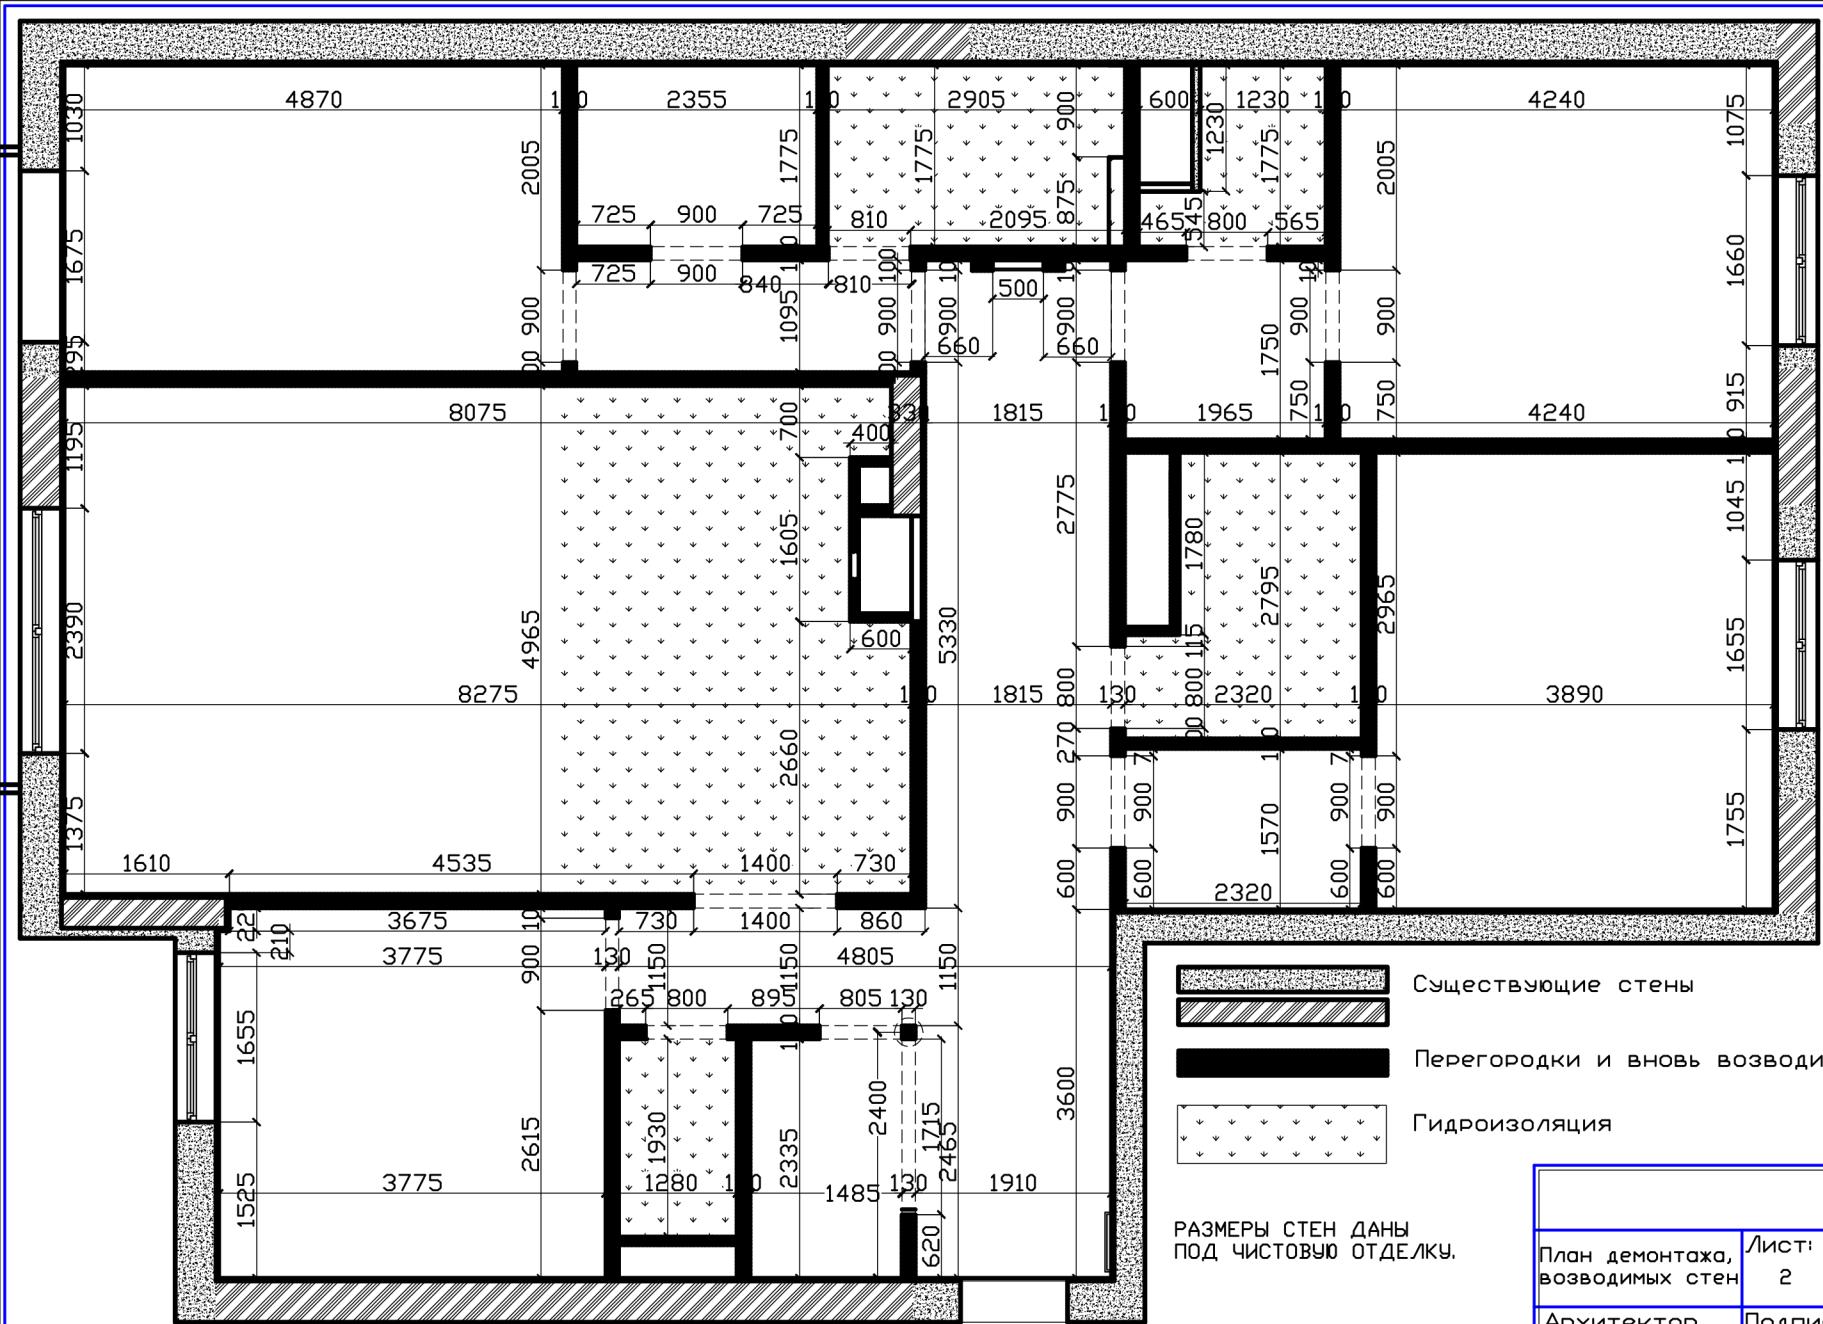

#### Существующие стены

## Перегородки и вновь возводимые стены

## Гидроизоляция

РАЗМЕРЫ СТЕН ДАНЫ  
ПОД ЧИСТОВУЮ ОТДЕЛКУ.


План демонтажа, возводимых стен	Лист: 2	Листов: 27
Архитектор	Подпись	Дата:
Дедловская Л.		24.12.19

## Примечания

1. Установить подвесные унитазы, обеспечить доступ к гребенкам.
2. Установить фильтры тонкие и грубые на стадии монтажа гребенок.
3. Потолок выровнять при необходимости Ротбандом на минимальной высоте от перекрытия – 3–5см вместе с электрикой.
4. Вызвать специалистов по вентиляции, пожарной сигнализации и акустике(если необходимо) на стадии монтажа стен для согласования их требований к монтажу.
5. Электрощиток вывести на стене прихожей в простенке, отведенном для него.
6. Предусмотреть выключение одним тумблером всей электрики, кроме холодильника и сигнализации.
7. Предусмотреть гидроизоляцию в мокрых зонах (кухня, ванная).
8. Толщина вновь возводимых стен 130мм (под чистовую отделку) Уточнить.
- В случае изменения толщины стен учитывать разницу в размере стен.
9. Ревизионные люки расположить, рассчитав высоту расположения гребенок так, чтобы люк был в уровне швов плитки.
10. Дверные проемы в комнаты сделать высотой 2450мм от чистого пола.
11. Проем в гостиную 2600 оформляется доборами и наличниками

## Предусмотреть звукоизоляцию пола

План демонтажа, возводимых стен	Лист: 2	Листов: 27
Архитектор	Подпись	Дата:
Дедловская Л.		24.12.19

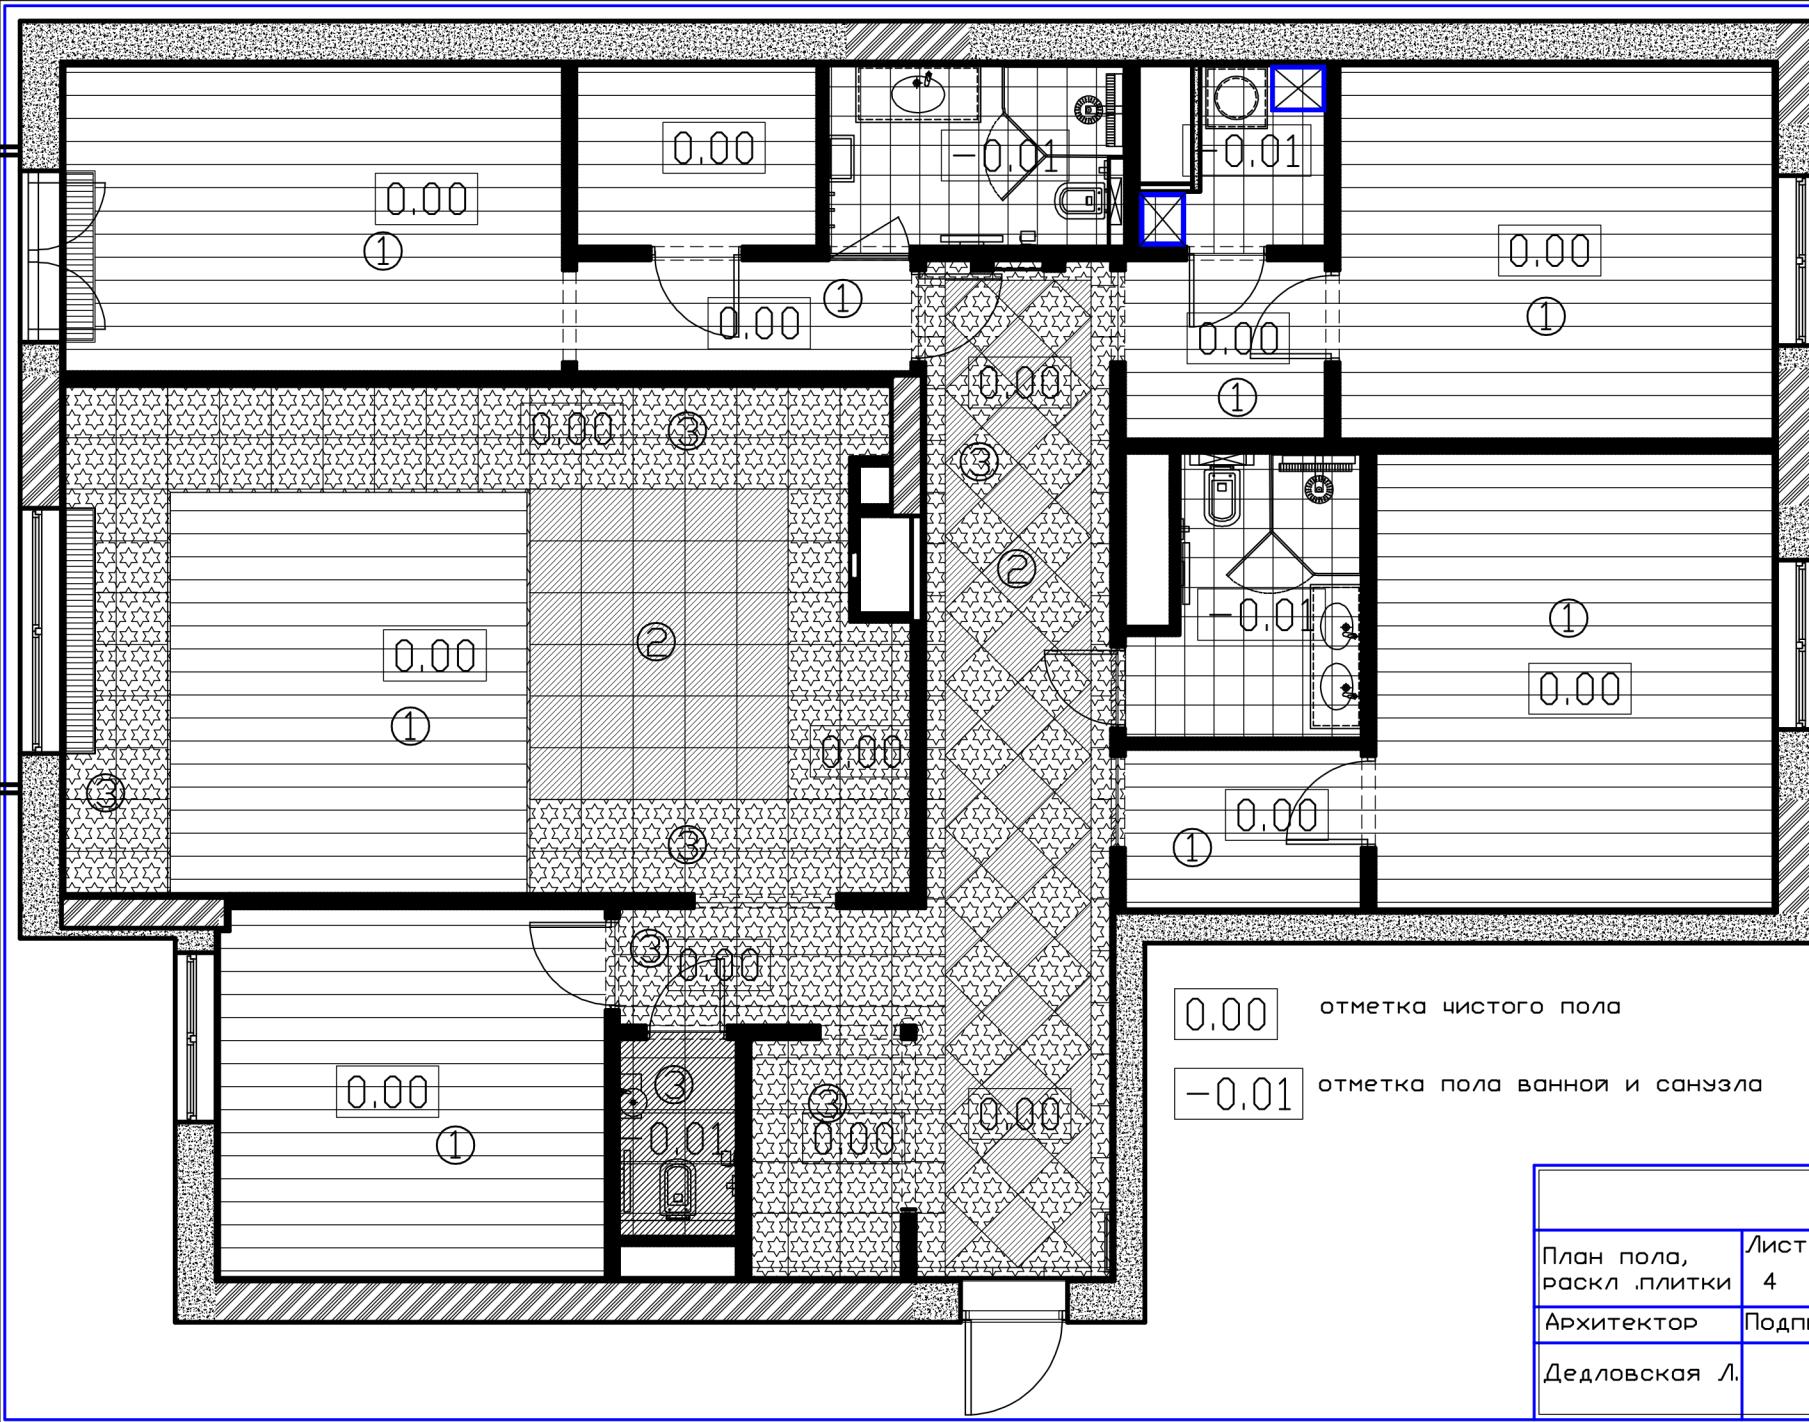

0.00 отметка чистого пола

-0.01 отметка пола ванной и санузла

План пола, раскл. плитки	Лист: 4	Листов: 27
Архитектор	Подпись	Дата:
Дедловская Л.		24.12.19

Примечание. Установить конвекторы под окнами по индивидуальным размерам.

Конвекторы заказывать только после дополнительных обмеров. Произвести расчет теплоотдачи оборудования перед заказом.

**[0.00]** отметка чистого пола

**[-0.01]** отметка пола ванной и санузла

Шов между паркетной доской и плиткой обрабатывается металлической полосой таврового сечения 14 мм. Общая длина шва 17м. Цвет никель

#### Спецификация материалов

① Паркетная доска - 90м<sup>2</sup> (+3%)


② Random Crema 510x510 - 16м<sup>2</sup>(+3%)


③ Random Divina Bronze 510x510 - 43м<sup>2</sup>(+3%)

Плинтус - всего 133 м.п. для всей квартиры

Раскладка - 17 м.п. всего для проемов

План пола, раскл .плитки	Лист: 4-1	Листов: 27
Архитектор	Подпись	Дата:
Дедловская Л.		24.12.19

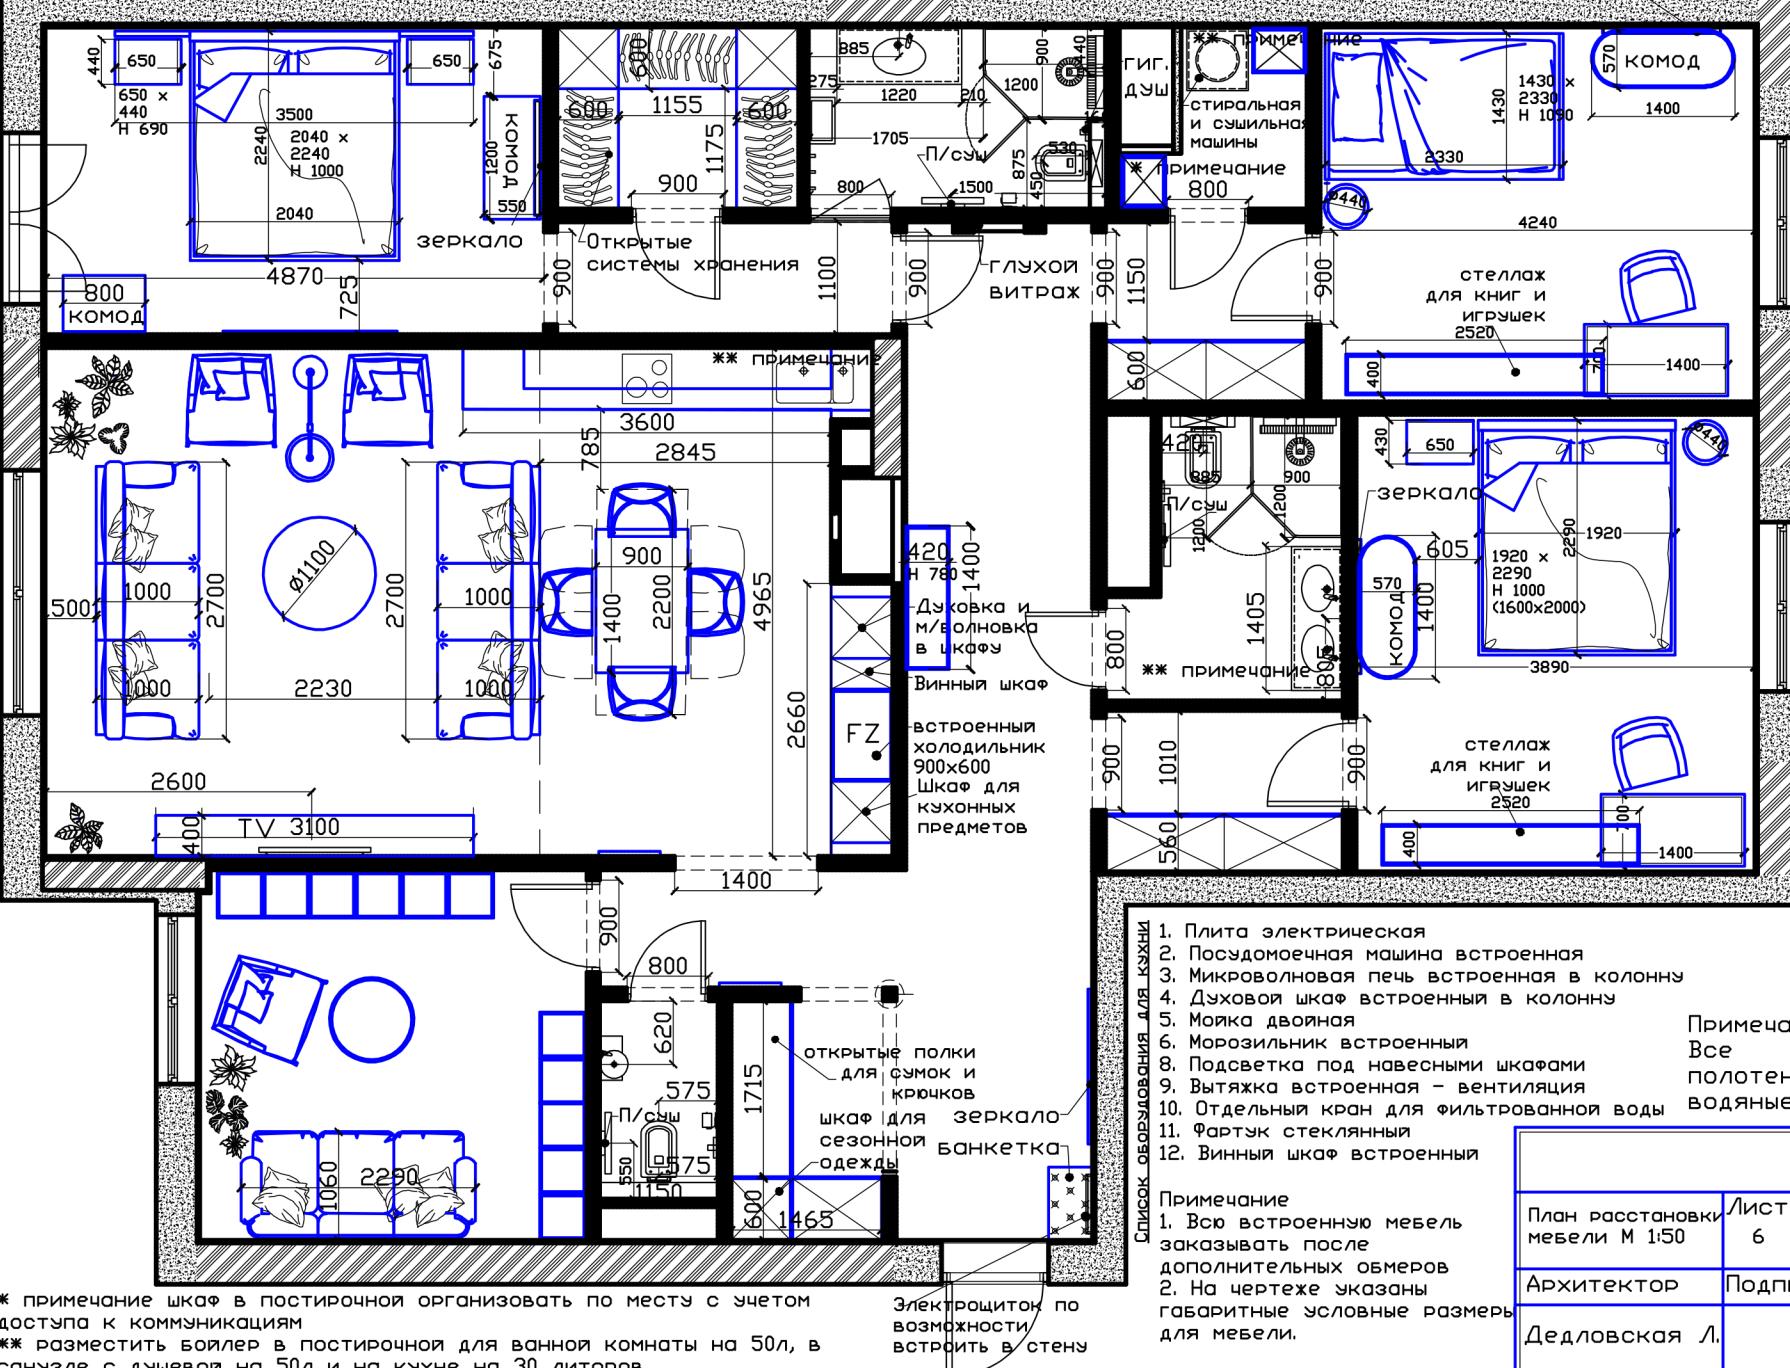

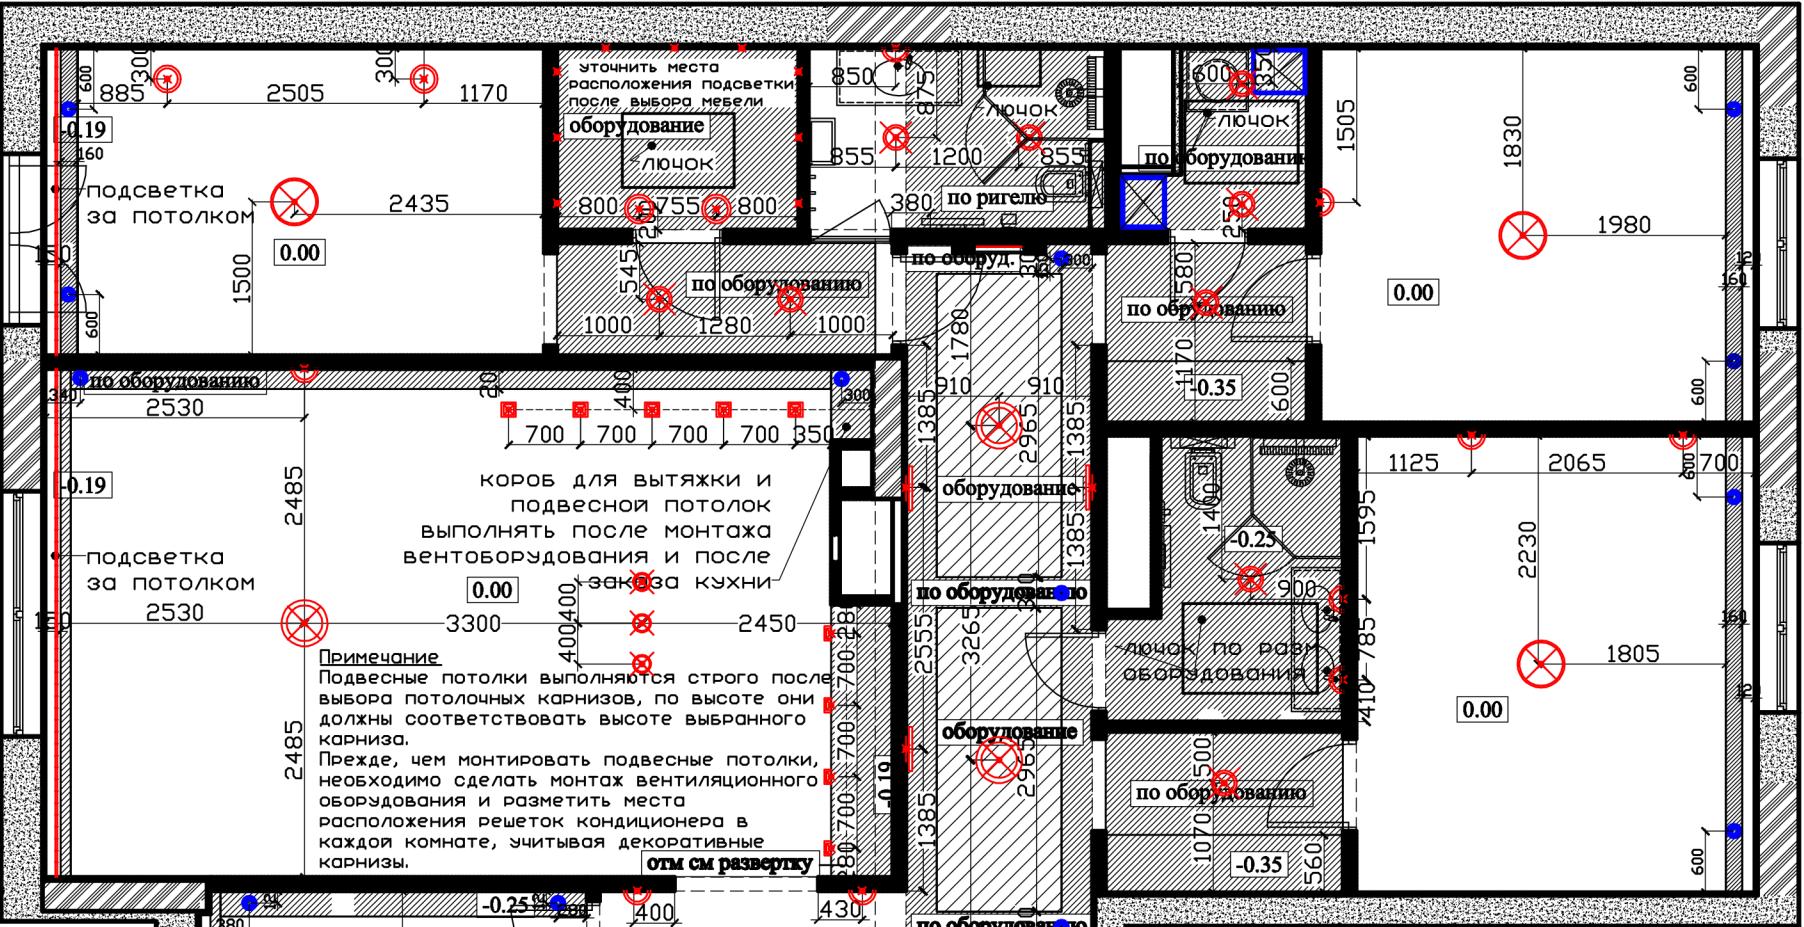


Уточнить количество светильников на кухне над встроенной мебелью

- Светильник подвесной
  - Светильник встро. точечн.
  - Светильн. накладн. потолочн.
  - Подсветка для картин
  - Бра (настенный светильник)
  - Светодиодная лента

Выровненный потолок  
Отметка 0,00

Подвесной потолок  
От 0.00 отметка  
указана на плане

План потолка. Отм., привязки светильников	Лист: 8	Листов: 27
Архитектор	Подпись	Дата:
Дедловская Л.		24.12.19

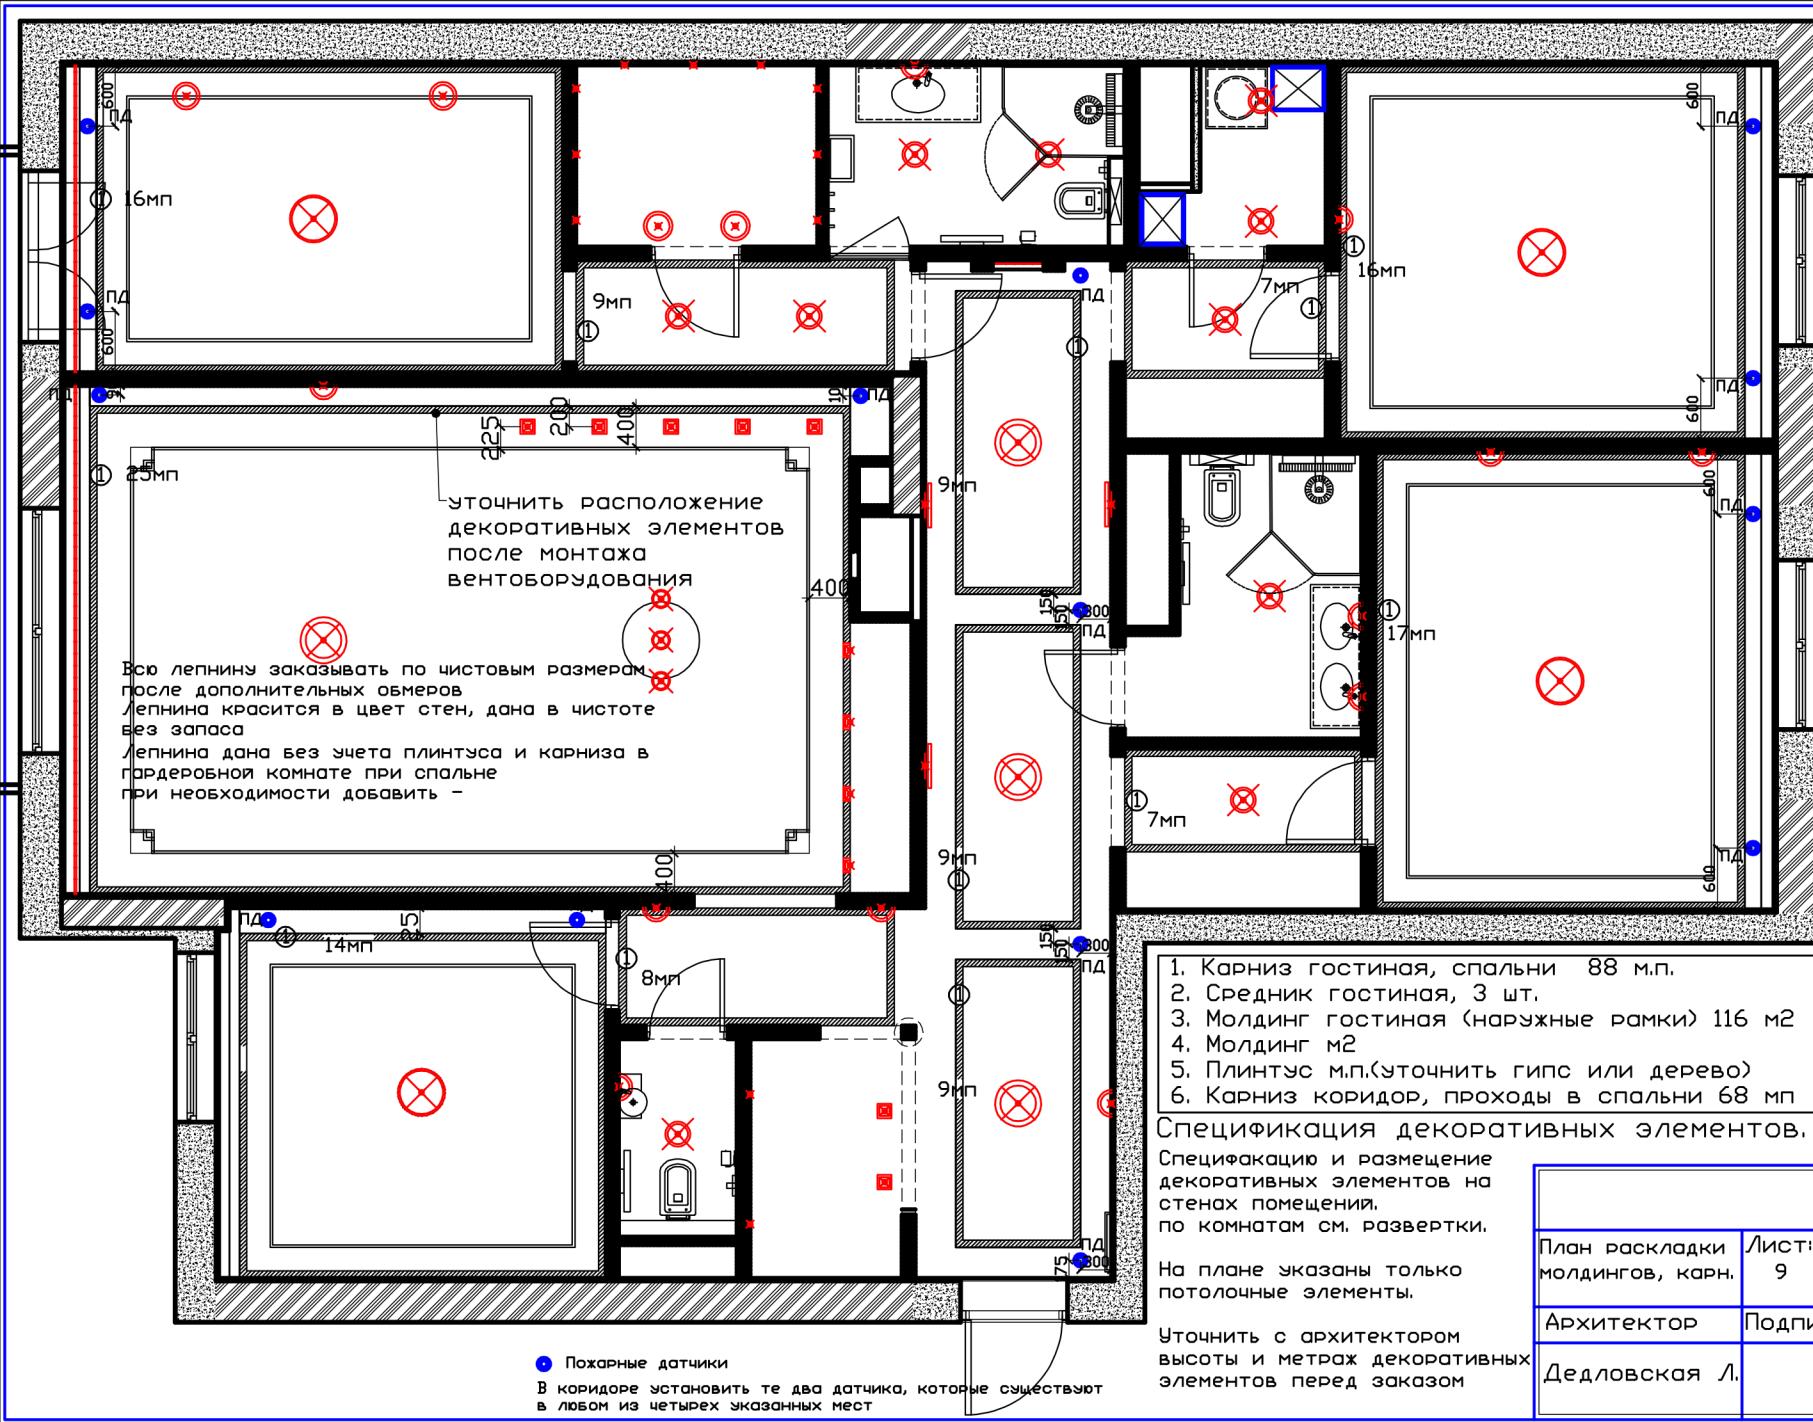

План раскладки молдингов, карн.	Лист: 9	Листов: 27
Архитектор	Подпись	Дата:
Дедловская Л.		24.12.19

## Ведомость отделки помещений

N	Помещение S-м2/Р-м.п.	Пол		Потолок		Стены	
		Вид отделки	М2	Вид отделки	М2	Вид отделки	М2
1.	Прихожая-коридор 18м2/23,6м.п.	Керамогранитная плитка	18	Подвесной потолок Подвесной потолок, декор	17,1 0,9	Покраска Dulux	43,7
2.	Гостиная-столовая 40м2/27,3мп	Керамогранитная плитка Паркетная доска	26,2 13,8	Выровненный потолок Подвесной потолок, декор	36,9м2 3,1м2	Покраска Dulux	71,9
3.	Кабинет 13,3м2/14,6м.п.	Паркетная доска	13,3	Выровненный потолок Подвесной потолок, декор	12,9 0,4	Покраска Dulux	37,5
4.	Спальня 16,4м2/17м.п.	Паркетная доска	16,4	Выровненный потолок декор Подвесной потолок, декор	13,9 2,5	Обои декоративные	44,4
5.	Гардеробная/спальня 3,1м2/7	Паркетная доска	3,1	Выровненный потолок	3,1	Покраска Dulux	18,7
6.	Коридор в спальню 2,9м2/7,5м.п.	Паркетная доска	2,9	Выровненный потолок	2,9	Покраска Dulux	12,9
7.	Ванная комната 5м2/9,4м.п.	Керамогранитная плитка	5	Натяжной потолок	5	Керамогранитная плитка	26,3
8.	Детский санузел 5,6м2/10,3м.п.	Керамогранитная плитка	5,6	Натяжной потолок	5,6	Керамогранитная плитка	28,8
9.	Коридор в детск-1 3,6м2/7,8м.п.	Паркетная доска	3,6	Выровненный потолок, декор Подвесной потолок	2,4 1,2	Покраска Dulux	18,6
10.	Детская-1 17,3м2/16,7м.п.	Паркетная доска	17,3	Выровненный потолок, декор	17,3	Обои декоративные	44,3
11.	Детская-2 15,5м2/15,8м.п.	Паркетная доска	15,5	Выровненный потолок, декор	15,5	Обои декоративные	41,5
12.	Коридор в детск-2 3,4м2/7,4м.п.	Паркетная доска	3,4	Выровненный потолок Подвесной потолок	2,3 1,1	Покраска Dulux	15,0
13.	Постирочная 2,5м2/7,2м.п.	Керамогранитная плитка	2,5	Выровненный потолок	2,5	Керамогранитная плитка	19,5
14.	Гостевой санузел 2,2м2/6,2м.п.	Керамогранитная плитка	2,2	Натяжной потолок	2,2	Керамогранитная плитка	16,5
15.	Гардероб/прихожая 3,7м2/7,8м.п.	Керамогранитная плитка	3,7	Подвесной потолок	3,7	Покраска Dulux	13,2
16.	Коридор-гостиная 3,3м2/8м.п.	Керамогранитная плитка	3,3	Подвесной потолок	3,3	Покраска Dulux	9,5

Перекрытие выравнивается Ротбандом, подвесной потолок в кухне выполняются из Г/К листов.

План размещения выключателей	Лист: 10	Листов: 27
Архитектор	Подпись	Дата:
Дедловская Л.		24.12.19